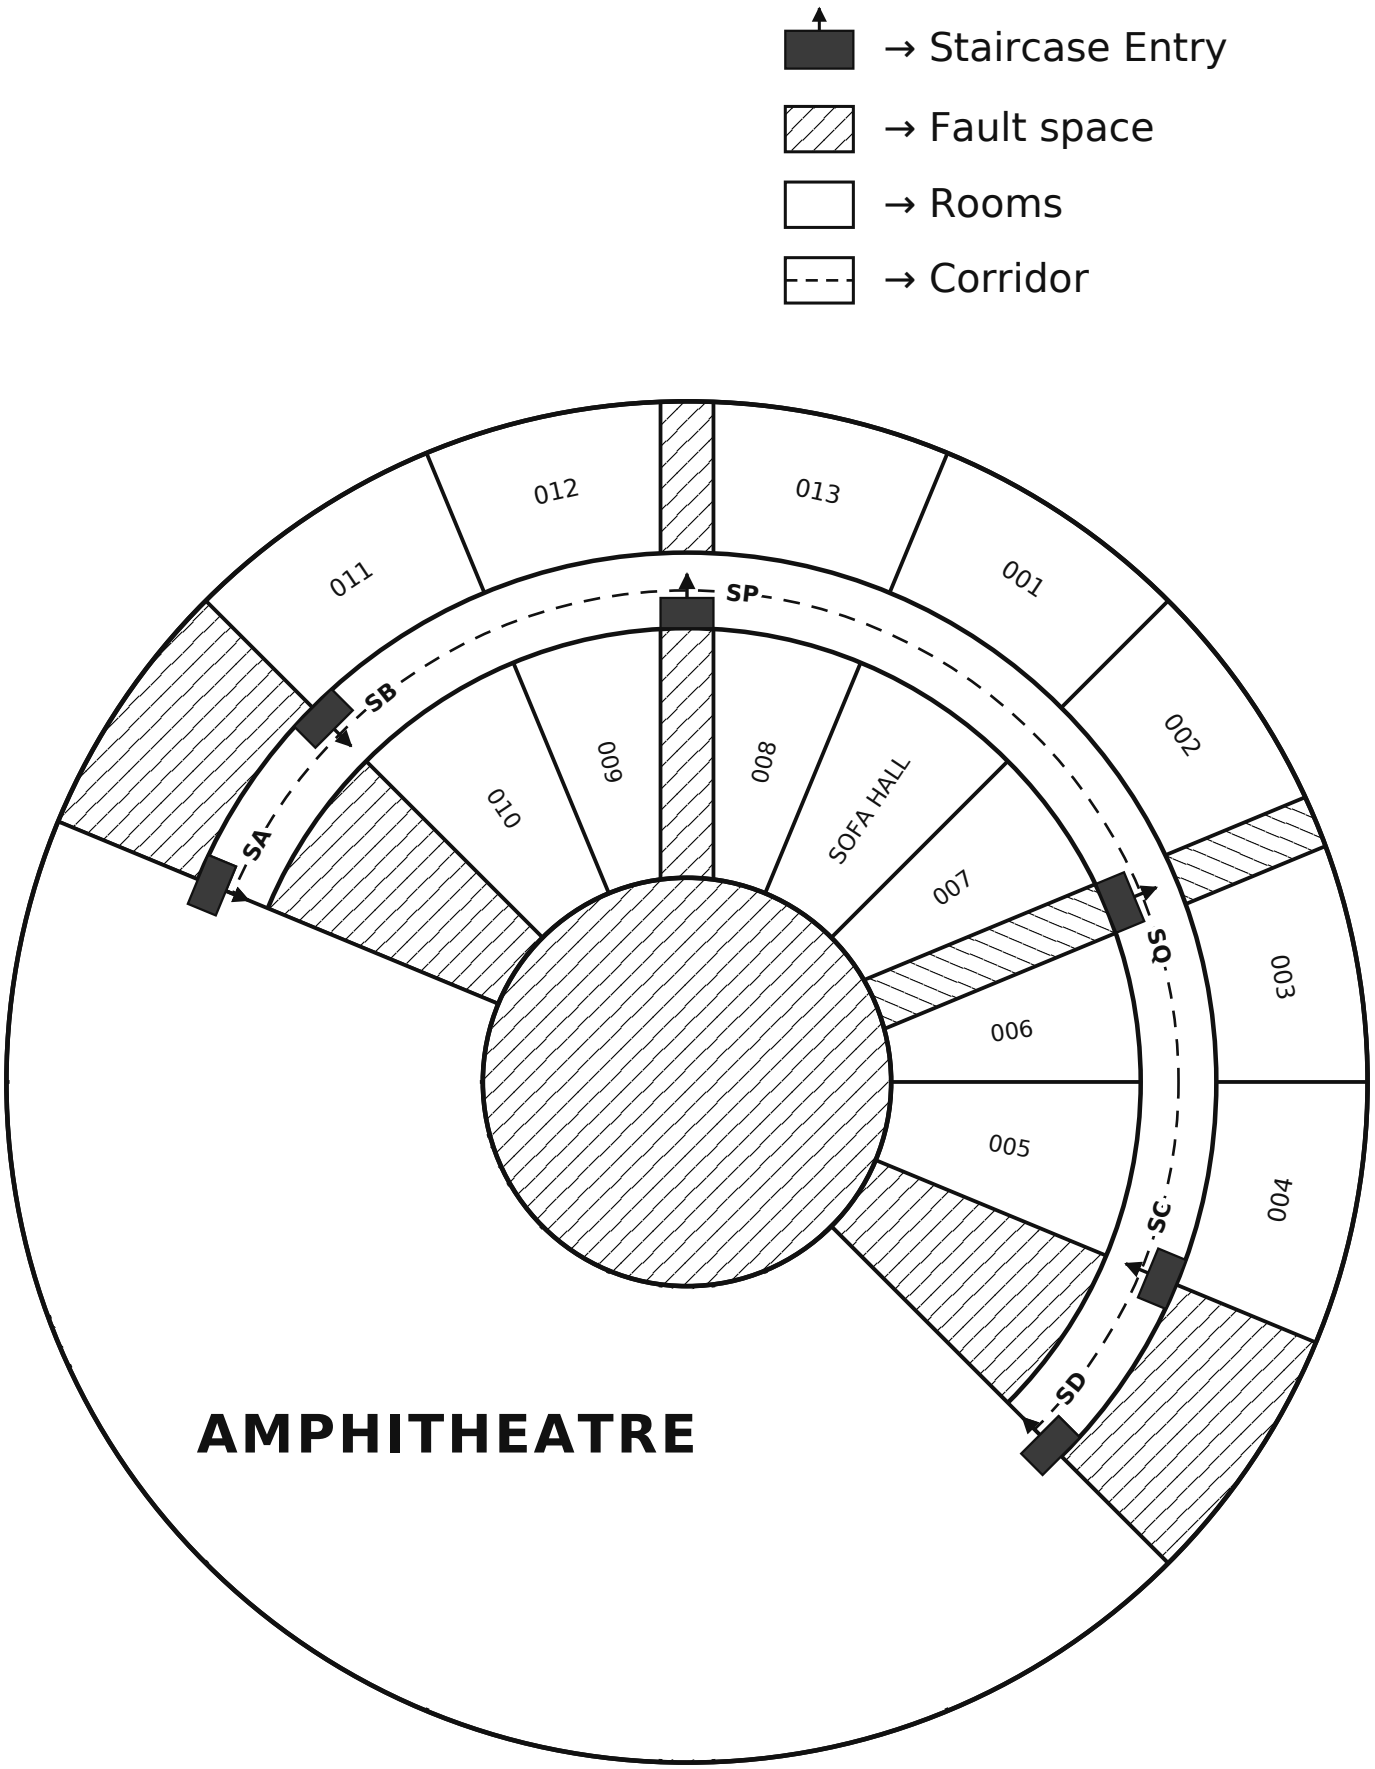
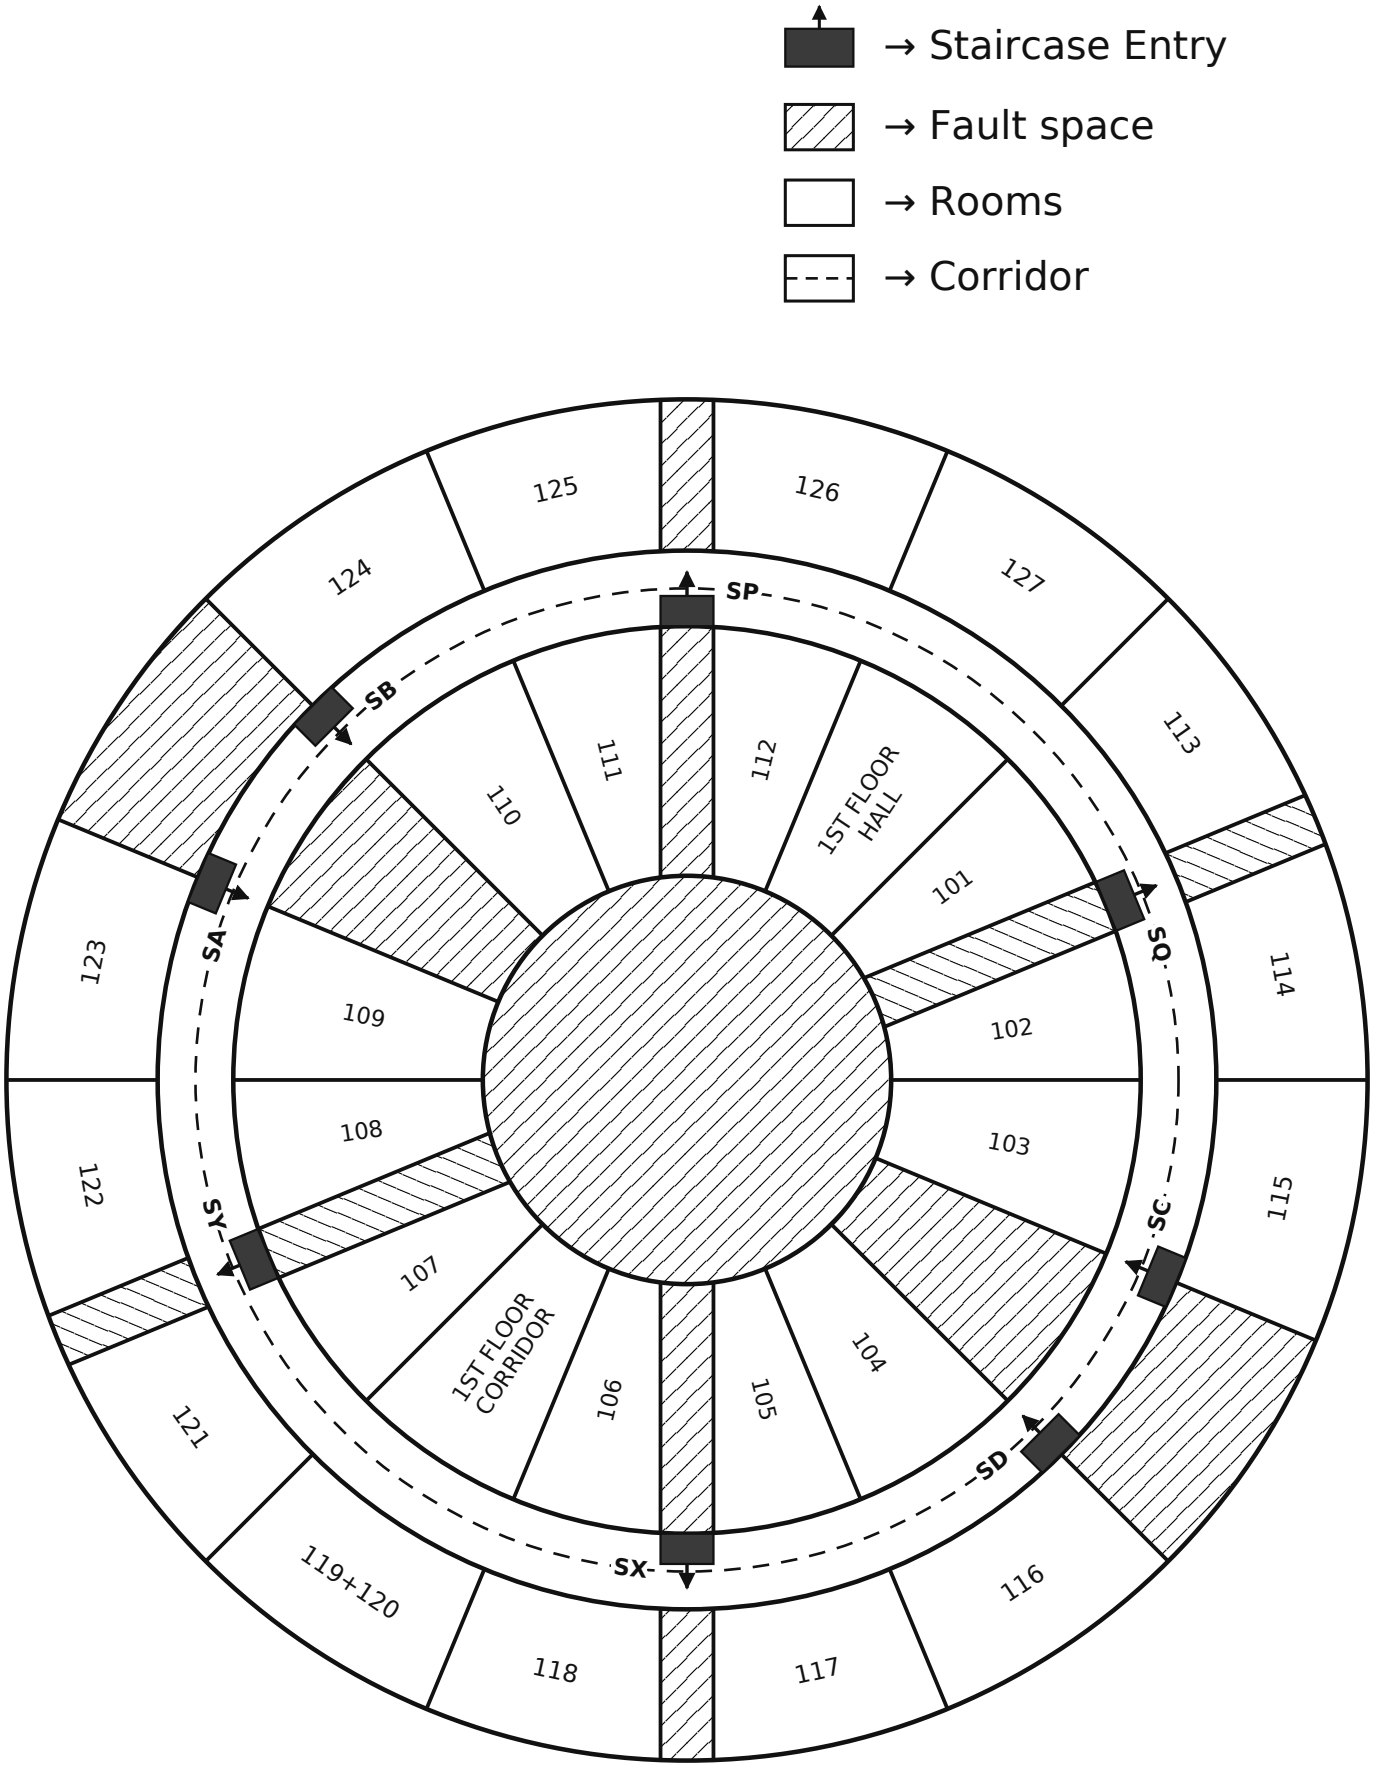
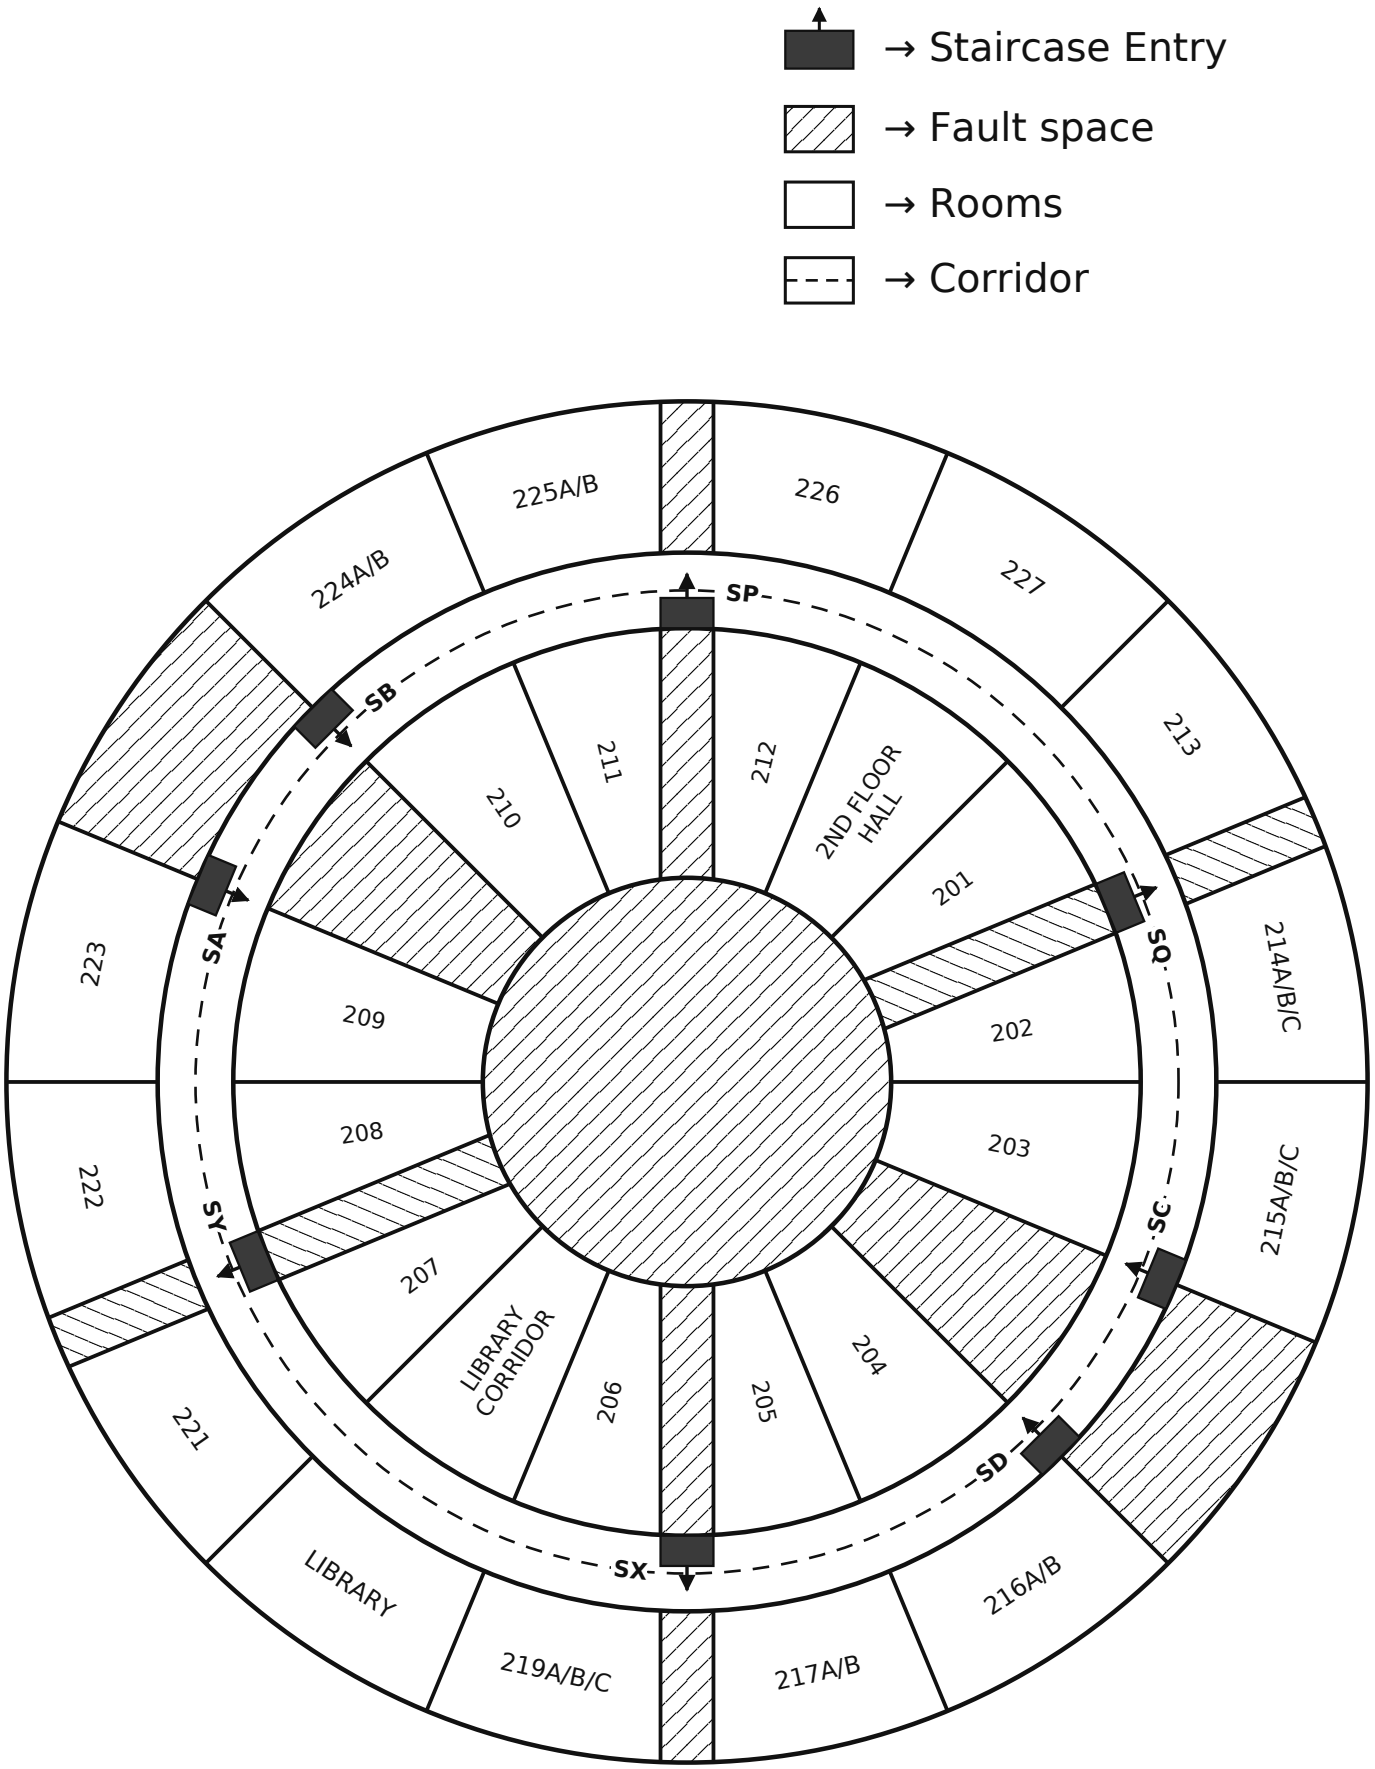
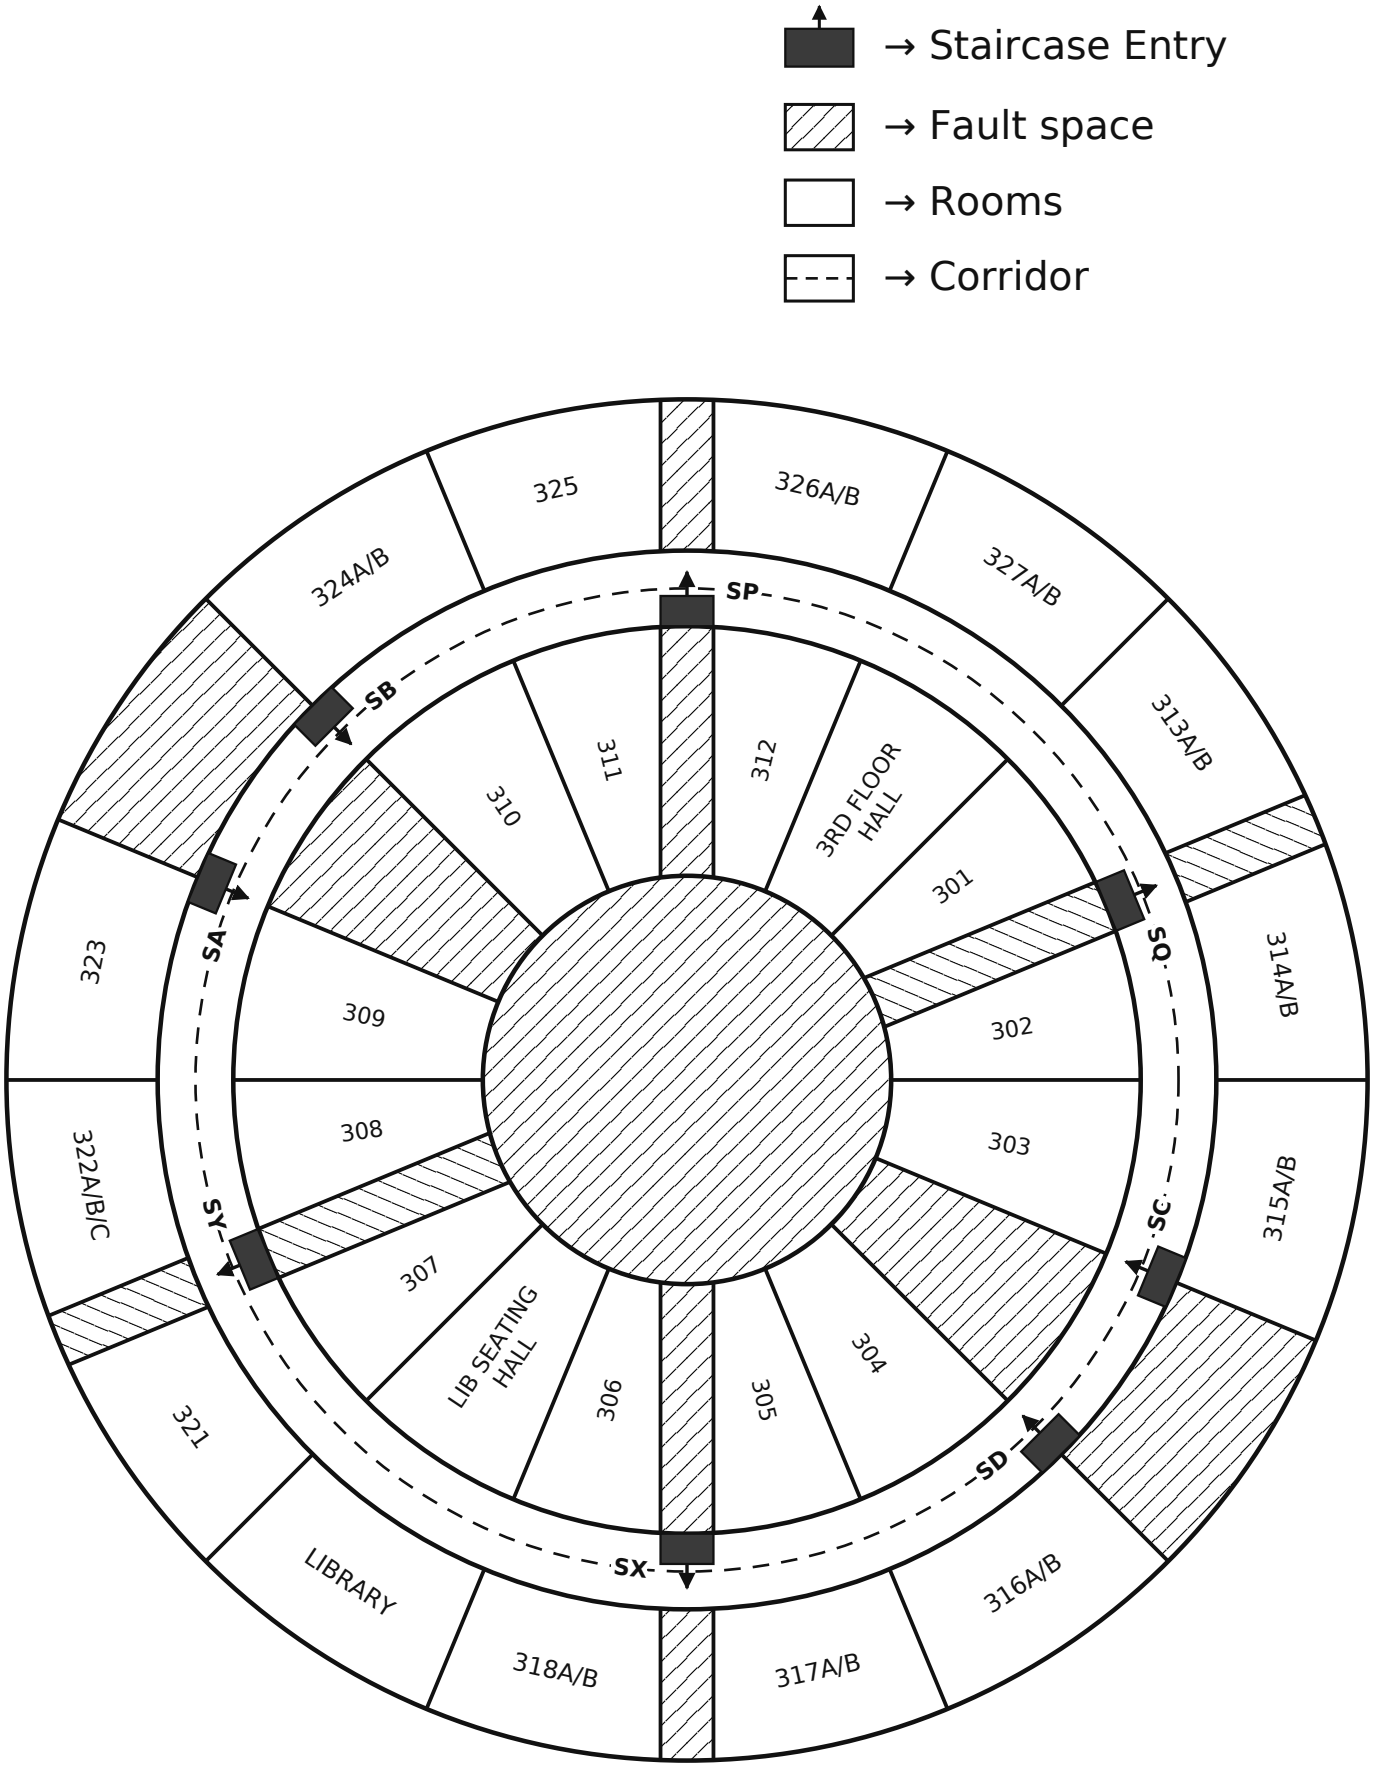
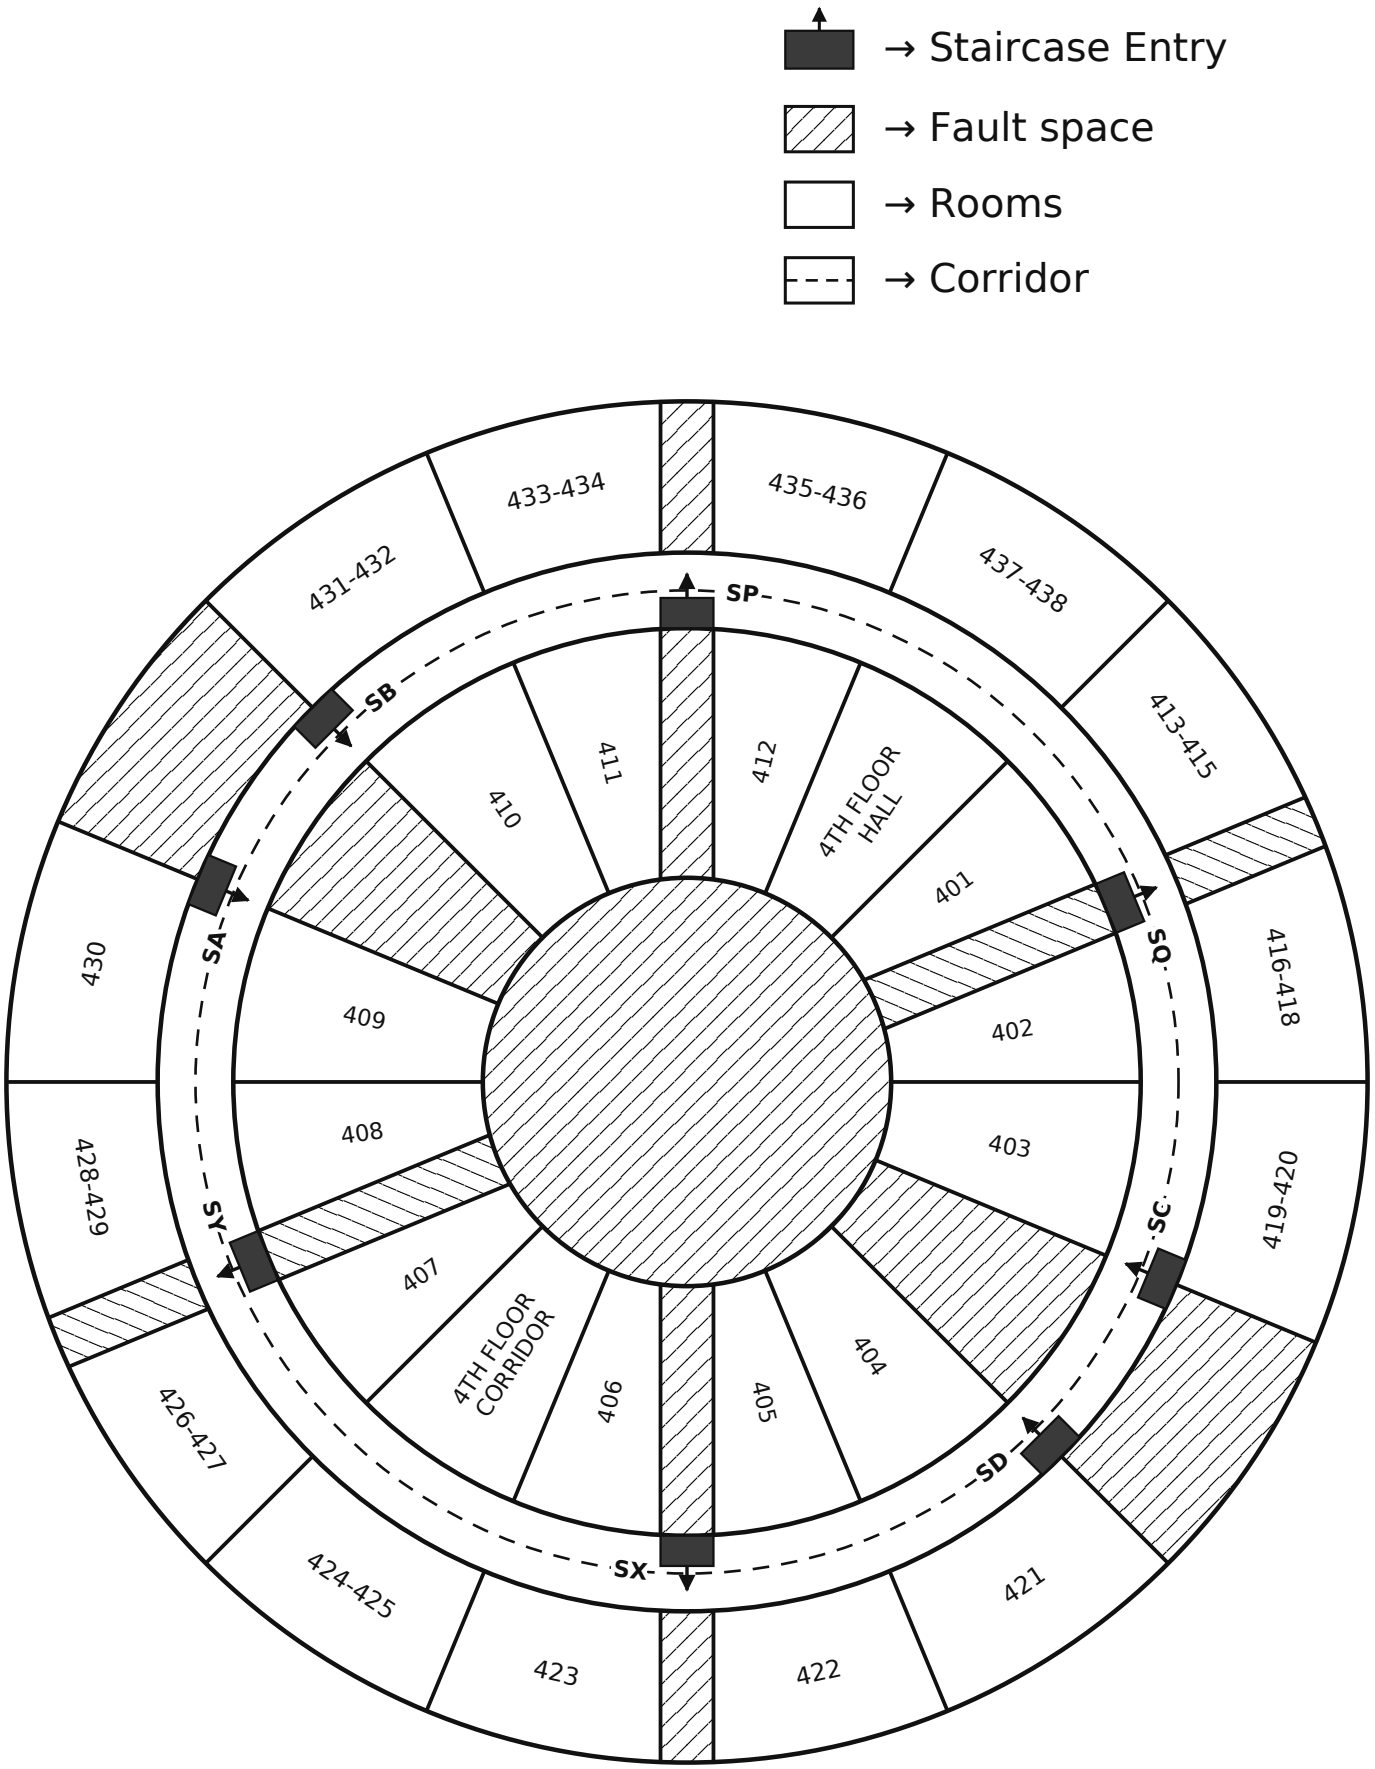

→ Staircase Entry
→ Fault space
→ Rooms
→ Corridor
011
012
013
001
002
003
004
005
006
007
SOFA HALL
008
009
010
SP
SA
SB
SC
SD
AMPHITHEATRE


→ Staircase Entry
→ Fault space
→ Rooms
→ Corridor
SP
SB
SA
SY
SX
SD
SC
SQ
1ST FLOOR HALL
1ST FLOOR CORRIDOR
101
102
103
104
105
106
107
108
109
110
111
112
113
114
115
116
117
118
119+120
121
122
123
124
125
126
127


→ Staircase Entry
→ Fault space
→ Rooms
→ Corridor
SP
SB
SA
SY
SX
SD
SC
SQ
224A/B
225A/B
226
227
213
214A/B/C
215A/B/C
216A/B
217A/B
219A/B/C
LIBRARY
221
222
223
210
211
212
2ND FLOOR HALL
201
202
203
204
205
206
LIBRARY CORRIDOR
207
208
209


→ Staircase Entry
→ Fault space
→ Rooms
→ Corridor
SP
SB
SA
SY
SX
SD
SC
SQ
324A/B
325
326A/B
327A/B
313A/B
314A/B
315A/B
316A/B
317A/B
318A/B
LIBRARY
321
322A/B/C
323
310
311
312
3RD FLOOR HALL
301
302
303
304
305
306
LIB SEATING HALL
307
308
309


→ Staircase Entry
→ Fault space
→ Rooms
→ Corridor
SP
SB
SA
SY
SX
SD
SC
SQ
431-432
433-434
435-436
437-438
413-415
416-418
419-420
421
422
423
424-425
426-427
428-429
430
410
411
412
4TH FLOOR HALL
401
402
403
404
405
406
4TH FLOOR CORRIDOR
407
408
409